

# GOBIERNO AUTÓNOMO DESCENTRALIZADO URDANETA.

## LEVANTAMIENTO PLANIMÉTRICO

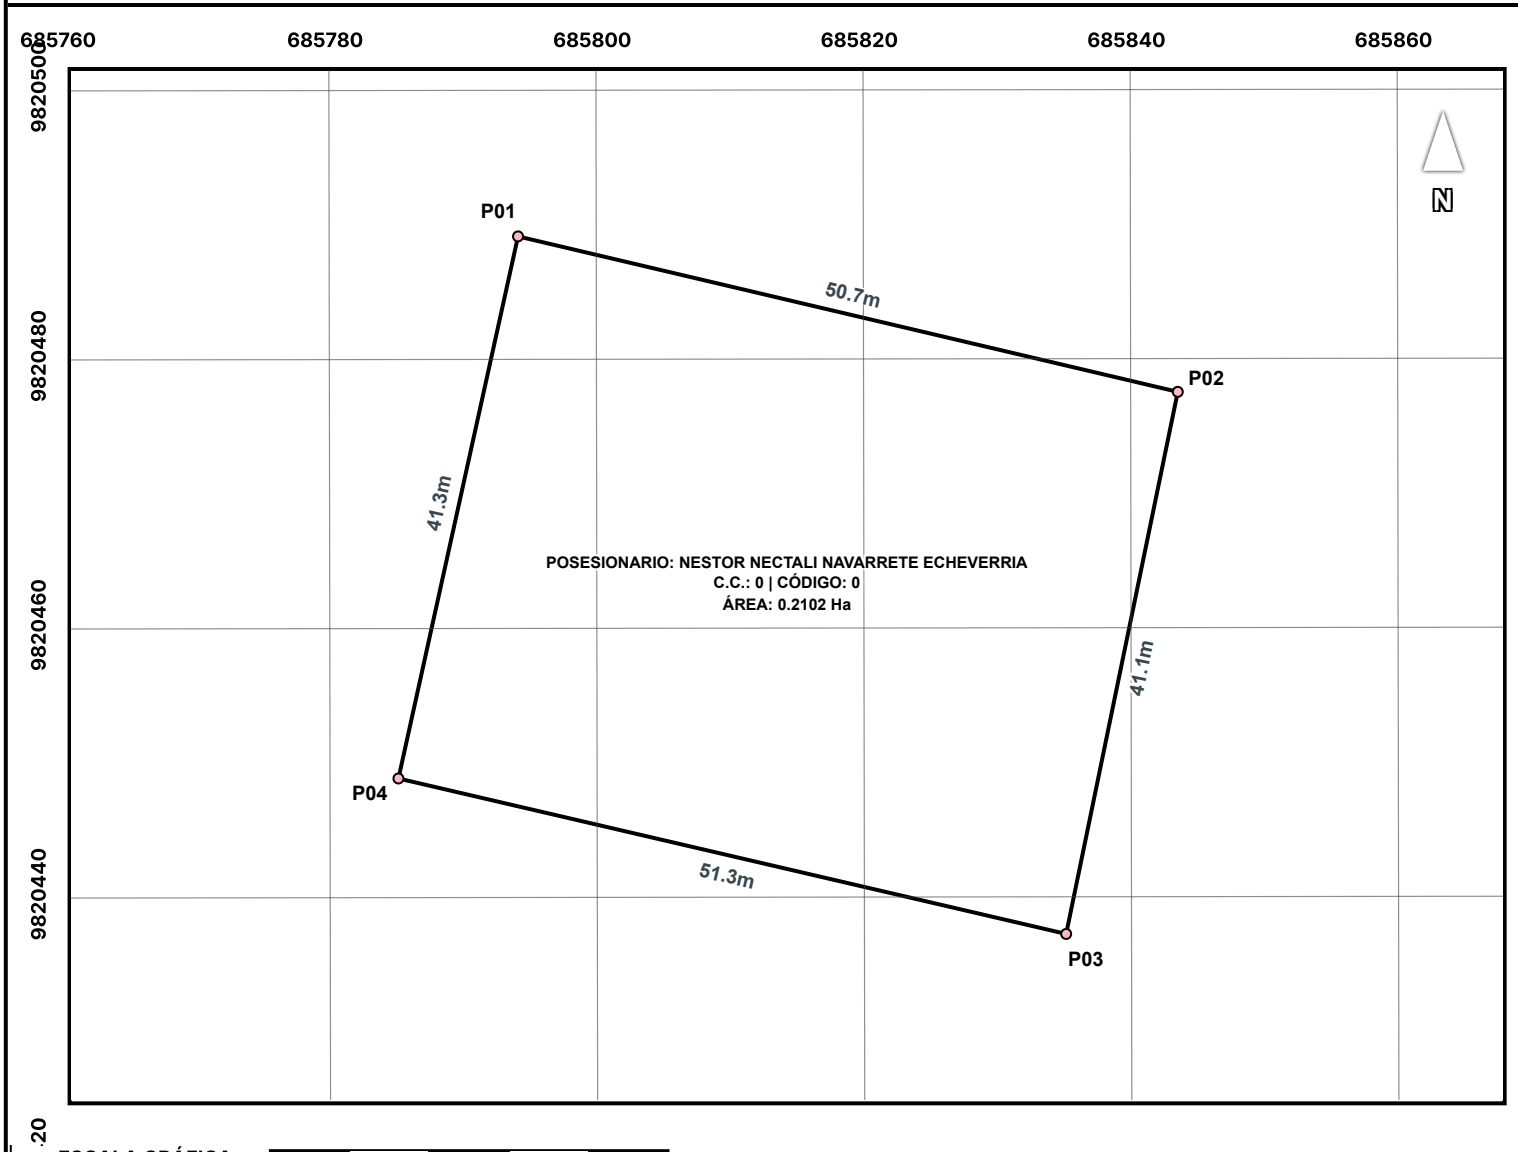


ESCALA GRÁFICA: 0 6 12 18 24 30 Metros

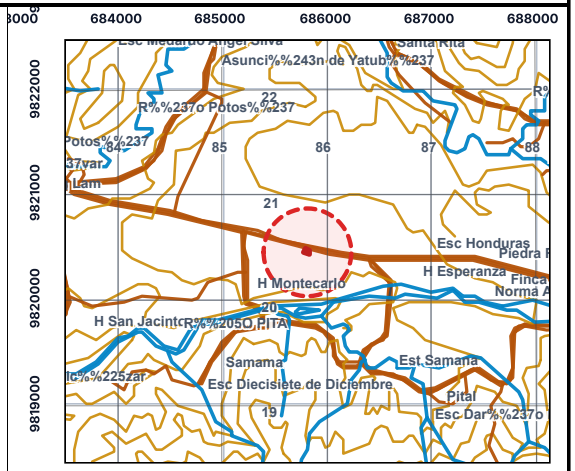


**UBICACIÓN:**

**CARTA TOPOGRÁFICA:** VENTANAS / CATARAMA / JUAN MONTALVO
**CÓDIGO:** NIV D1, 3789 IV / NIV D3, 3789 III / NIV F1, 3788 IV
**ESCALA:** 1:50000

**POSESIONARIO:**

NESTOR NECTALI NAVARRETE ECHEVERRIA
**C.C.:** 0

**CODIGO CATASTRAL:**

0

| **PROVINCIA:** | **CANTÓN:** |
|---|---|
| LOS RIOS | URDANETA |

**PARROQUIA:**

CATARAMA - URDANETA - PIJULLO

**SECTOR:**

RURAL

**NOMBRE DEL PREDIO:**

SIN NOMBRE

| **FECHA:** | **ÁREA:** | **ESCALA:** | **COORDENADAS PLANAS:** |
|---|---|---|---|
| 15/10/2026 | 0.2102 Ha | ~ 1:500 | SISTEMA DE COORDENADAS: WGS 1984 UTM ZONE 17S<br>PROYECCIÓN: TRANSVERSE MERCATOR<br>DATUM: WGS 1984 |

| **RESP. TÉCNICO:** | **REVISADO Y APROBADO POR:** |
|---|---|
| | Ing. Mauricio Basantes Rodriguez |

# INFORME DE LINDERACIÓN

| PROVINCIA: | CANTÓN: | PARROQUIA: | SECTOR: |
|---|---|---|---|
| Los Rios | Urdaneta | Catarama | Rural |

| NOMBRES DEL POSESIONARIO | NOMBRE DEL PREDIO | CÓDIGO CATASTRAL |
|---|---|---|
| NESTOR NECTALI NAVARRETE ECHEVERRIA<br>C.C.: 0 | SIN NOMBRE | 0 |

| PUNTOS | COORDENADAS PLANAS UTM W.G.S.-84 | | VERTICE DESDE-HASTA | DISTANCIA (M) | RUMBO | COLINDANTES |
|---|---|---|---|---|---|---|
| | X | Y | | | | |
| P01 | 685794.2 | 9820489.2 | P01 - P02 | 41.1 | S 11° 47' 14" W | - |
| P02 | 685843.5 | 9820477.5 | P02 - P03 | 51.3 | N 76° 54' 19" W | - |
| P03 | 685835.1 | 9820437.3 | P03 - P04 | 41.3 | N 12° 36' 28" E | - |
| P04 | 685785.1 | 9820448.9 | P04 - P01 | 50.7 | S 76° 37' 5" E | - |

# DESCRIPCIÓN DE LINDEROS

**COLINDANTE NORTE**

Del P01 al P02 con una distancia de 41.1 m, Rumbo S 11° 47' 14" W

**COLINDANTE SUR**

Del P03 al P04 con una distancia de 41.3 m, Rumbo N 12° 36' 28" E

**COLINDANTE ESTE**

Del P02 al P03 con una distancia de 51.3 m, Rumbo N 76° 54' 19" W


**COLINDANTE OESTE**


Del P04 al P01 con una distancia de 50.7 m, Rumbo S 76° 37' 5" E

| RESPONSABILIDAD TÉCNICA | REVISADO Y APROBADO POR: |
|---|---|
| | Ing. Mauricio Basantes Rodriguez |

# GOBIERNO AUTÓNOMO DESCENTRALIZADO URDANETA.

## LEVANTAMIENTO PLANIMÉTRICO

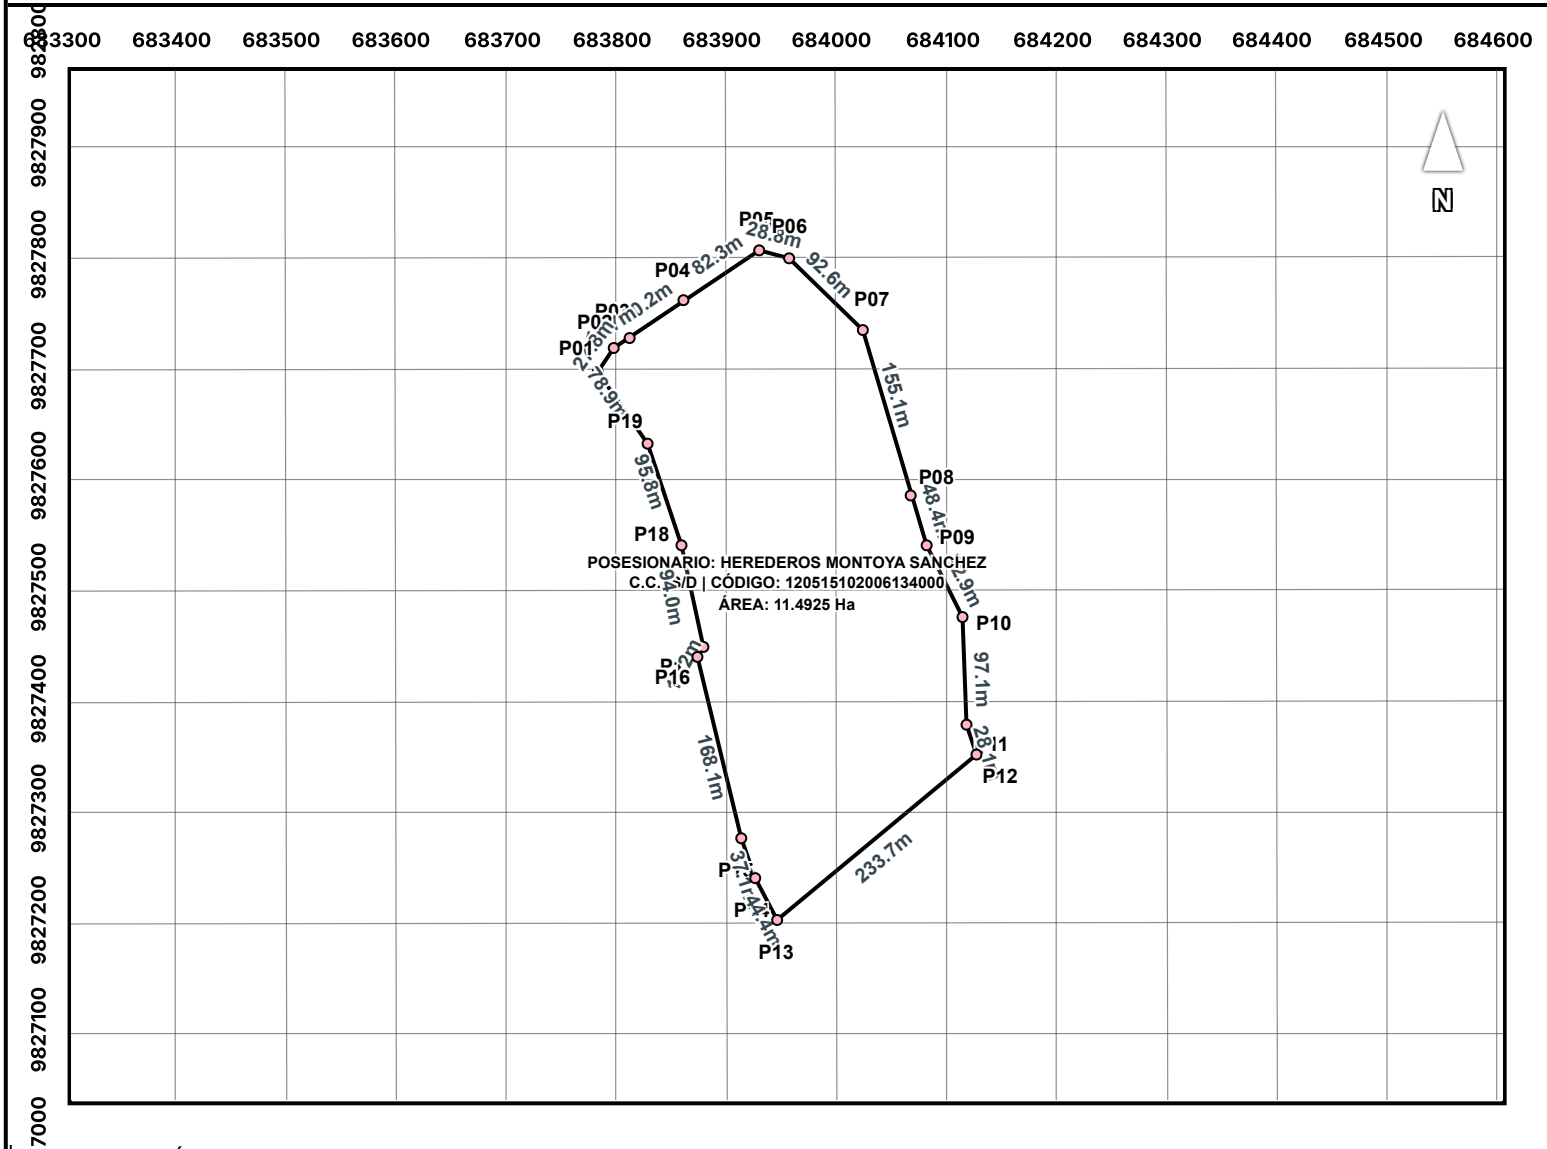

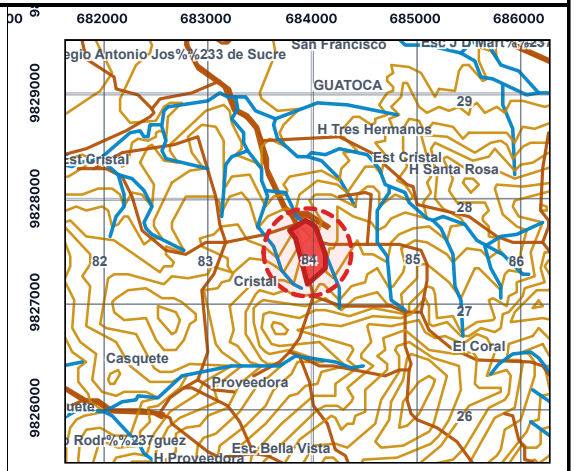
**UBICACIÓN:**

**CARTA TOPOGRÁFICA:** VENTANAS / CATARAMA / JUAN MONTALVO
**CÓDIGO:** NIV D1, 3789 IV / NIV D3, 3789 III / NIV F1, 3788 IV
**ESCALA:** 1:50000

**POSESIONARIO:**

HEREDEROS MONTOYA SANCHEZ
**C.C.:** S/D

**CODIGO CATASTRAL:**

120515102006134000

| **PROVINCIA:** | **CANTÓN:** |
|---|---|
| LOS RIOS | URDANETA |

**PARROQUIA:**

CATARAMA - URDANETA - PIJULLO

**SECTOR:**

CRISTAL ALTO

**NOMBRE DEL PREDIO:**

SIN NOMBRE

**ESCALA GRÁFICA:** 0 100 200 300 400 500Metros

| **FECHA:** | **ÁREA:** | **ESCALA:** | **COORDENADAS PLANAS:** |
|---|---|---|---|
| 15/10/2026 | 11.4925 Ha | ~ 1:6100 | SISTEMA DE COORDENADAS: WGS 1984 UTM ZONE 17S<br>PROYECCIÓN: TRANSVERSE MERCATOR<br>DATUM: WGS 1984 |

| **RESP. TÉCNICO:** | **REVISADO Y APROBADO POR:** |
|---|---|
| | Ing. Mauricio Basantes Rodriguez |

# INFORME DE LINDERACIÓN

| PROVINCIA: | CANTÓN: | PARROQUIA: | SECTOR: |
|---|---|---|---|
| Los Rios | Urdaneta | Catarama | CRISTAL ALTO |

| NOMBRES DEL POSESIONARIO | NOMBRE DEL PREDIO | CÓDIGO CATASTRAL |
|---|---|---|
| HEREDEROS MONTOYA SANCHEZ<br>C.C.: S/D | SIN NOMBRE | 120515102006134000 |

| PUNTOS | COORDENADAS PLANAS UTM W.G.S.-84 | | VERTICE DESDE-HASTA | DISTANCIA (M) | RUMBO | COLINDANTES |
|---|---|---|---|---|---|---|
| | X | Y | | | | |
| P01 | 683783.1 | 9827696.4 | P01 - P02 | 27.8 | N 34° 54' 6" E | - |
| P02 | 683798.9 | 9827719.1 | P02 - P03 | 15.7 | N 57° 22' 58" E | - |
| P03 | 683812.2 | 9827727.6 | P03 - P04 | 60.2 | N 55° 45' 3" E | - |
| P04 | 683861.9 | 9827761.5 | P04 - P05 | 82.3 | N 56° 0' 12" E | - |
| P05 | 683930.2 | 9827807.5 | P05 - P06 | 28.8 | S 74° 54' 50" E | - |
| P06 | 683958.0 | 9827800.0 | P06 - P07 | 92.6 | S 45° 27' 4" E | - |
| P07 | 684024.0 | 9827735.0 | P07 - P08 | 155.1 | S 16° 5' 44" E | - |
| P08 | 684067.0 | 9827586.0 | P08 - P09 | 48.4 | S 18° 3' 45" E | - |
| P09 | 684082.0 | 9827540.0 | P09 - P10 | 72.9 | S 26° 55' 31" E | - |
| P10 | 684115.0 | 9827475.0 | P10 - P11 | 97.1 | S 2° 21' 24" E | - |
| P11 | 684119.0 | 9827378.0 | P11 - P12 | 28.1 | S 16° 32' 1" E | - |
| P12 | 684127.0 | 9827351.0 | P12 - P13 | 233.7 | S 50° 23' 3" W | - |
| P13 | 683947.0 | 9827202.0 | P13 - P14 | 44.4 | N 29° 7' 27" W | - |
| P14 | 683925.4 | 9827240.8 | P14 - P15 | 37.1 | N 17° 24' 11" W | - |
| P15 | 683914.3 | 9827276.2 | P15 - P16 | 168.1 | N 13° 55' 53" W | - |
| P16 | 683873.8 | 9827439.4 | P16 - P17 | 11.2 | N 26° 33' 48" E | - |
| P17 | 683878.8 | 9827449.5 | P17 - P18 | 94.0 | N 11° 31' 53" W | - |
| P18 | 683860.1 | 9827541.5 | P18 - P19 | 95.8 | N 19° 0' 36" W | - |
| P19 | 683828.8 | 9827632.2 | P19 - P01 | 78.9 | N 35° 28' 55" W | - |
| | | | | | | |
| | | | | | | |
# DESCRIPCIÓN DE LINDEROS

## COLINDANTE NORTE

Del P01 al P02 con una distancia de 27.8 m, Rumbo N 34° 54' 6" E
Del P02 al P03 con una distancia de 15.7 m, Rumbo N 57° 22' 58" E
Del P03 al P04 con una distancia de 60.2 m, Rumbo N 55° 45' 3" E
Del P04 al P05 con una distancia de 82.3 m, Rumbo N 56° 0' 12" E
Del P05 al P06 con una distancia de 28.8 m, Rumbo S 74° 54' 50" E
Del P06 al P07 con una distancia de 92.6 m, Rumbo S 45° 27' 4" E

## COLINDANTE SUR

Del P12 al P13 con una distancia de 233.7 m, Rumbo S 50° 23' 3" W

## COLINDANTE ESTE

Del P07 al P08 con una distancia de 155.1 m, Rumbo S 16° 5' 44" E
Del P08 al P09 con una distancia de 48.4 m, Rumbo S 18° 3' 45" E
Del P09 al P10 con una distancia de 72.9 m, Rumbo S 26° 55' 31" E
Del P10 al P11 con una distancia de 97.1 m, Rumbo S 2° 21' 24" E
Del P11 al P12 con una distancia de 28.1 m, Rumbo S 16° 32' 1" E


## COLINDANTE OESTE


Del P13 al P14 con una distancia de 44.4 m, Rumbo N 29° 7' 27" W
Del P14 al P15 con una distancia de 37.1 m, Rumbo N 17° 24' 11" W
Del P15 al P16 con una distancia de 168.1 m, Rumbo N 13° 55' 53" W
Del P16 al P17 con una distancia de 11.2 m, Rumbo N 26° 33' 48" E
Del P17 al P18 con una distancia de 94.0 m, Rumbo N 11° 31' 53" W
Del P18 al P19 con una distancia de 95.8 m, Rumbo N 19° 0' 36" W
Del P19 al P01 con una distancia de 78.9 m, Rumbo N 35° 28' 55" W

| RESPONSABILIDAD TÉCNICA | REVISADO Y APROBADO POR: |
|---|---|
| | Ing. Mauricio Basantes Rodriguez |

# GOBIERNO AUTÓNOMO DESCENTRALIZADO URDANETA.

## LEVANTAMIENTO PLANIMÉTRICO

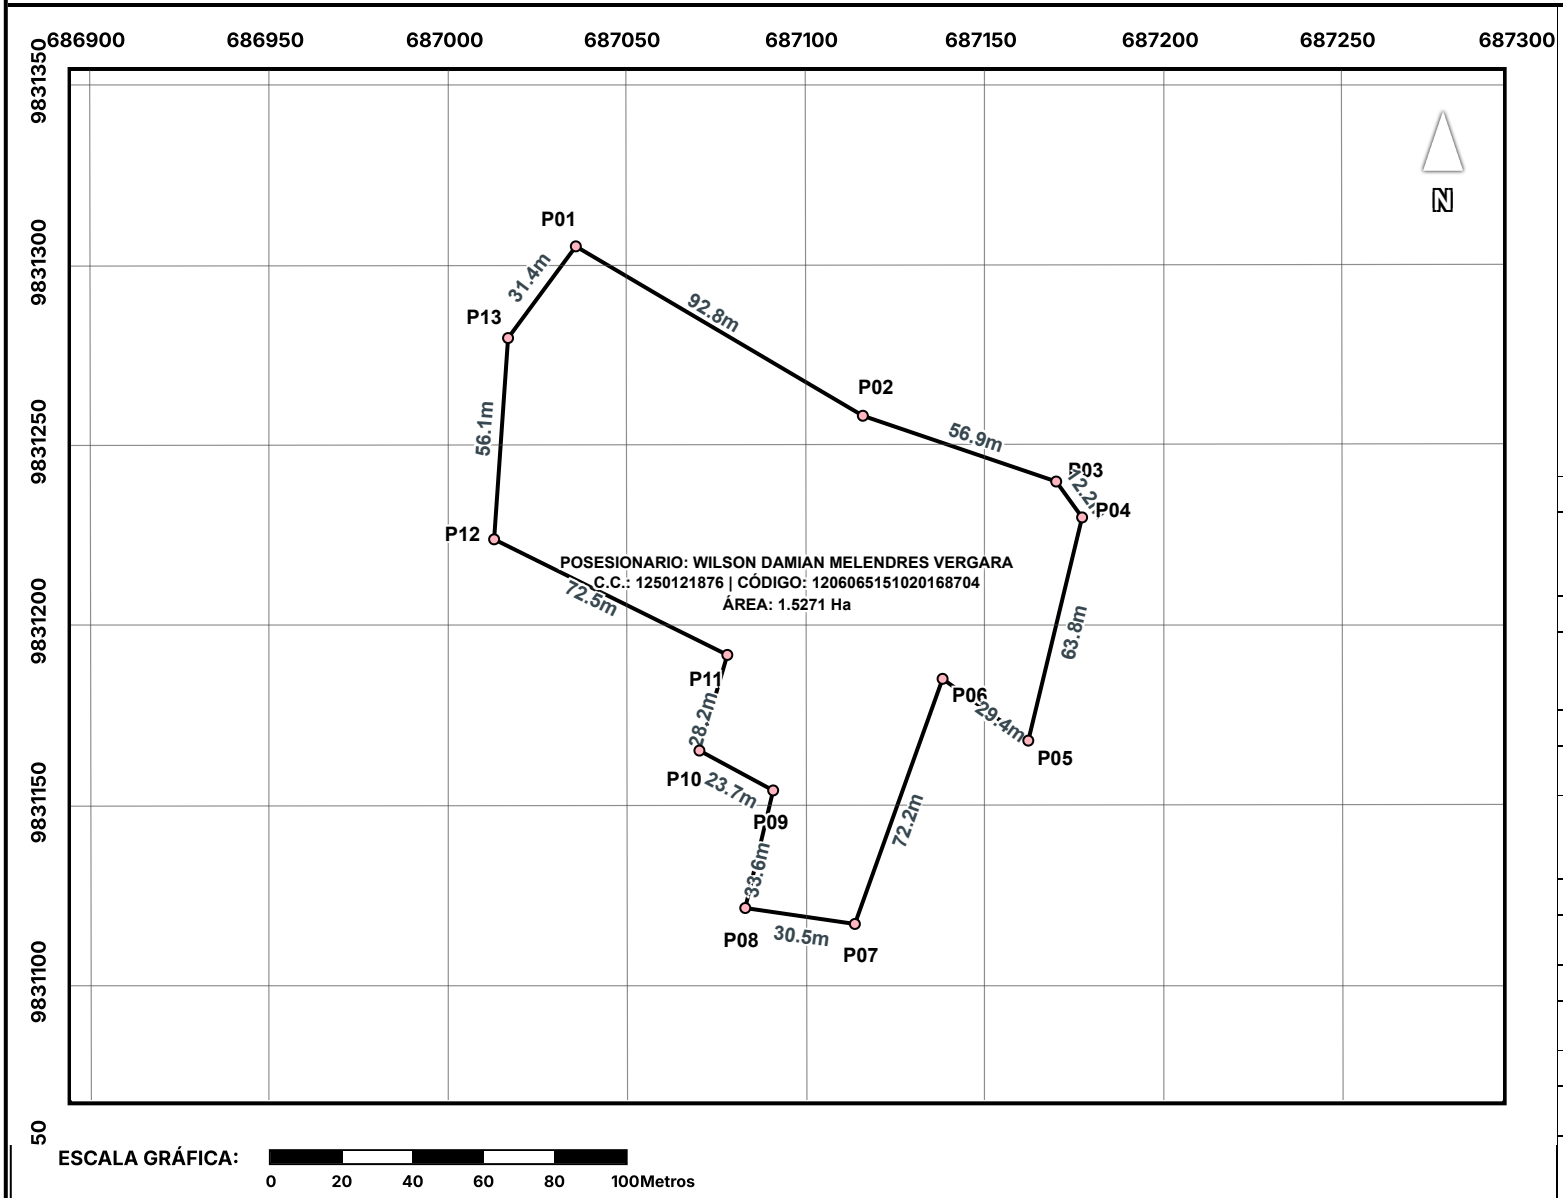

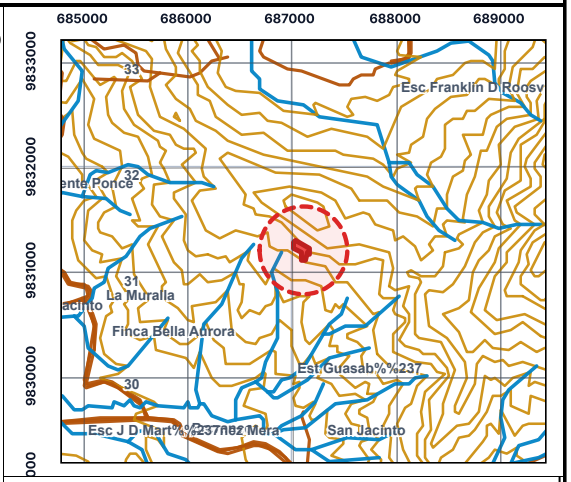
**UBICACIÓN:**

**CARTA TOPOGRÁFICA:** VENTANAS / CATARAMA / JUAN MONTALVO
**CÓDIGO:** NIV D1, 3789 IV / NIV D3, 3789 III / NIV F1, 3788 IV
**ESCALA:** 1:50000

**POSESIONARIO:**

WILSON DAMIAN MELENDRES VERGARA
**C.C.:** 1250121876

**CODIGO CATASTRAL:**

1206065151020168704

| **PROVINCIA:** | **CANTÓN:** |
|---|---|
| LOS RIOS | URDANETA |

**PARROQUIA:**

CATARAMA - URDANETA - PIJULLO

**SECTOR:**

LA INDUSTRIA

**NOMBRE DEL PREDIO:**

SIN NOMBRE

| **FECHA:** | **ÁREA:** | **ESCALA:** | **COORDENADAS PLANAS:** |
|---|---|---|---|
| 15/10/2026 | 1.5271 Ha | ~ 1:1900 | SISTEMA DE COORDENADAS: WGS 1984 UTM ZONE 17S<br>PROYECCIÓN: TRANSVERSE MERCATOR<br>DATUM: WGS 1984 |

| **RESP. TÉCNICO:** | **REVISADO Y APROBADO POR:** |
|---|---|
| | Ing. Mauricio Basantes Rodriguez |

# INFORME DE LINDERACIÓN

| PROVINCIA: | CANTÓN: | PARROQUIA: | SECTOR: |
|---|---|---|---|
| Los Rios | Urdaneta | Catarama | LA INDUSTRIA |

| NOMBRES DEL POSESIONARIO | NOMBRE DEL PREDIO | CÓDIGO CATASTRAL |
|---|---|---|
| WILSON DAMIAN MELENDRES VERGARA<br>C.C.: 1250121876 | SIN NOMBRE | 1206065151020168704 |

| PUNTOS | COORDENADAS PLANAS UTM W.G.S.-84 | | VERTICE DESDE-HASTA | DISTANCIA (M) | RUMBO | COLINDANTES |
|---|---|---|---|---|---|---|
| | X | Y | | | | |
| P01 | 687036.0 | 9831305.0 | P01 - P02 | 12.2 | S 34° 59' 31" E | - |
| P02 | 687116.0 | 9831258.0 | P02 - P03 | 63.8 | S 13° 36' 2" W | - |
| P03 | 687170.0 | 9831240.0 | P03 - P04 | 29.4 | N 54° 41' 20" W | - |
| P04 | 687177.0 | 9831230.0 | P04 - P05 | 72.2 | S 19° 54' 33" W | - |
| P05 | 687162.0 | 9831168.0 | P05 - P06 | 30.5 | N 82° 14' 11" W | - |
| P06 | 687138.0 | 9831185.0 | P06 - P07 | 33.6 | N 13° 23' 48" E | - |
| P07 | 687113.4 | 9831117.2 | P07 - P08 | 23.7 | N 62° 21' 27" W | - |
| P08 | 687083.2 | 9831121.3 | P08 - P09 | 28.2 | N 16° 30' 16" E | - |
| P09 | 687091.0 | 9831154.0 | P09 - P10 | 72.5 | N 63° 47' 19" W | - |
| P10 | 687070.0 | 9831165.0 | P10 - P11 | 56.1 | N 4° 5' 8" E | - |
| P11 | 687078.0 | 9831192.0 | P11 - P12 | 31.4 | N 37° 14' 5" E | - |
| P12 | 687013.0 | 9831224.0 | P12 - P13 | 92.8 | S 59° 33' 57" E | - |
| P13 | 687017.0 | 9831280.0 | P13 - P01 | 56.9 | S 71° 33' 54" E | - |

# DESCRIPCIÓN DE LINDEROS

## COLINDANTE NORTE

Del P01 al P02 con una distancia de 12.2 m, Rumbo S 34° 59' 31" E
Del P02 al P03 con una distancia de 63.8 m, Rumbo S 13° 36' 2" W

## COLINDANTE SUR

Del P05 al P06 con una distancia de 30.5 m, Rumbo N 82° 14' 11" W
Del P06 al P07 con una distancia de 33.6 m, Rumbo N 13° 23' 48" E
Del P07 al P08 con una distancia de 23.7 m, Rumbo N 62° 21' 27" W

## COLINDANTE ESTE

Del P03 al P04 con una distancia de 29.4 m, Rumbo N 54° 41' 20" W
Del P04 al P05 con una distancia de 72.2 m, Rumbo S 19° 54' 33" W

## COLINDANTE OESTE

Del P08 al P09 con una distancia de 28.2 m, Rumbo N 16° 30' 16" E
Del P09 al P10 con una distancia de 72.5 m, Rumbo N 63° 47' 19" W
Del P10 al P11 con una distancia de 56.1 m, Rumbo N 4° 5' 8" E
Del P11 al P12 con una distancia de 31.4 m, Rumbo N 37° 14' 5" E
Del P12 al P13 con una distancia de 92.8 m, Rumbo S 59° 33' 57" E
Del P13 al P01 con una distancia de 56.9 m, Rumbo S 71° 33' 54" E

| RESPONSABILIDAD TÉCNICA | REVISADO Y APROBADO POR: |
|---|---|
| | Ing. Mauricio Basantes Rodriguez |