

GOBIERNO AUTÓNOMO DESCENTRALIZADO URDANETA.

LEVANTAMIENTO PLANIMÉTRICO

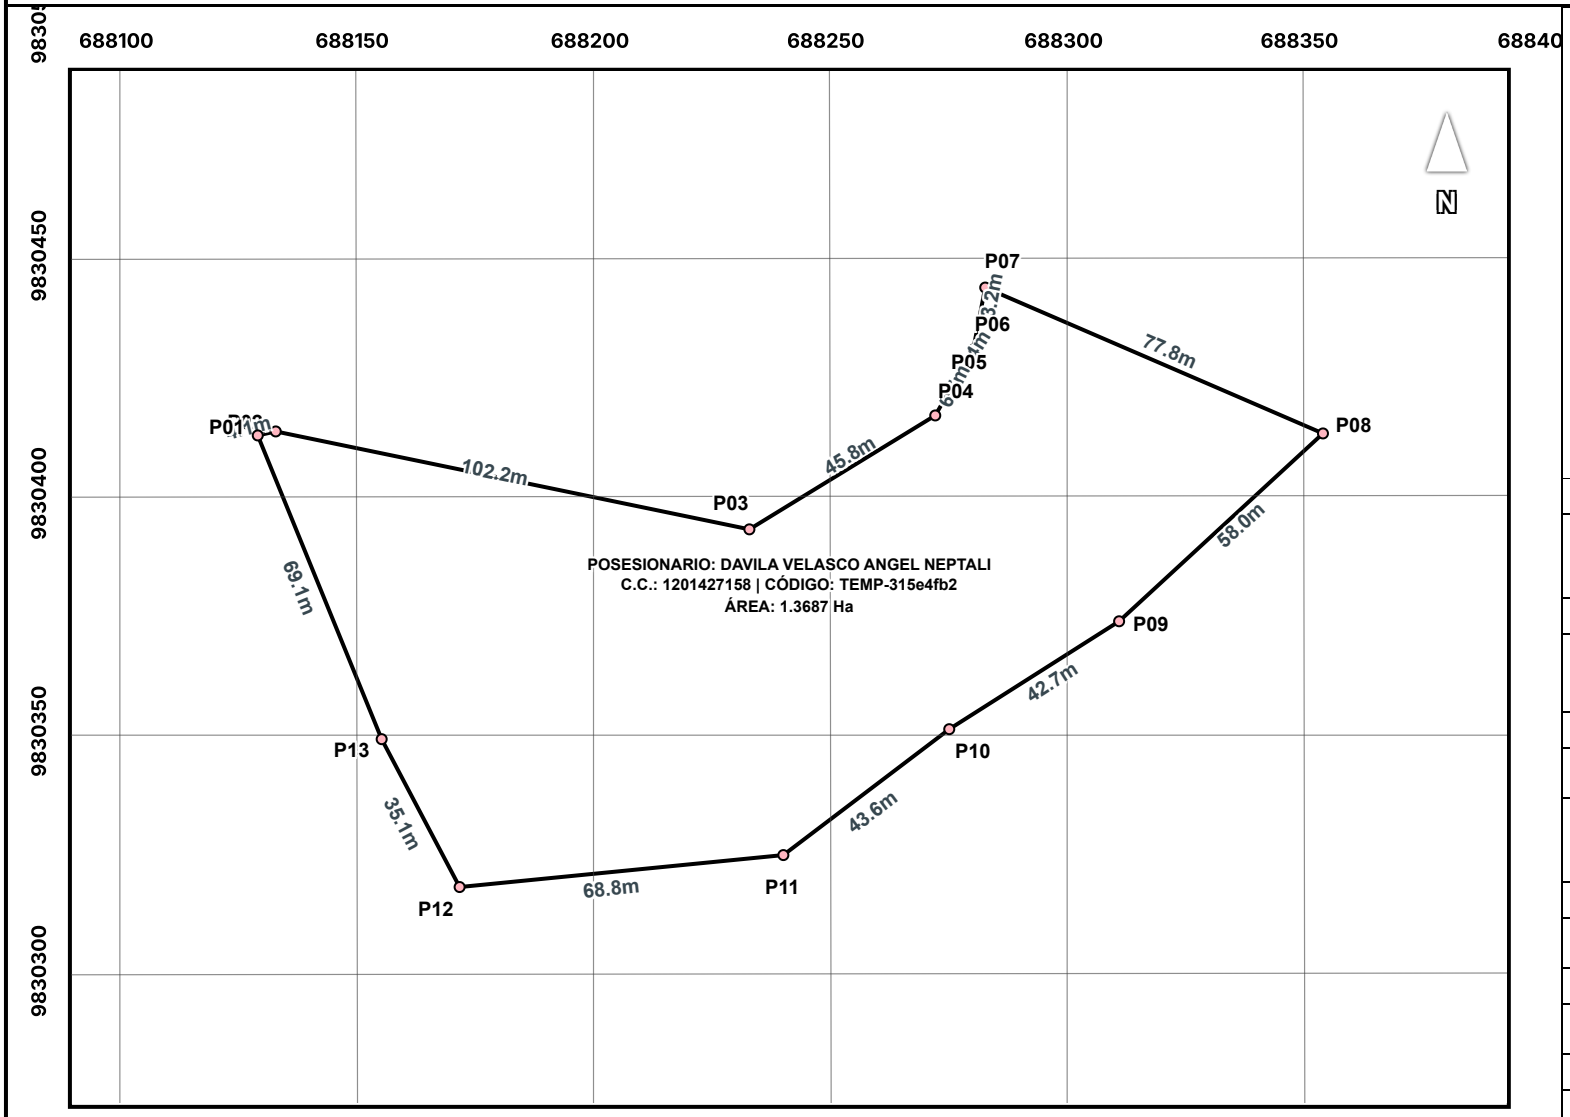

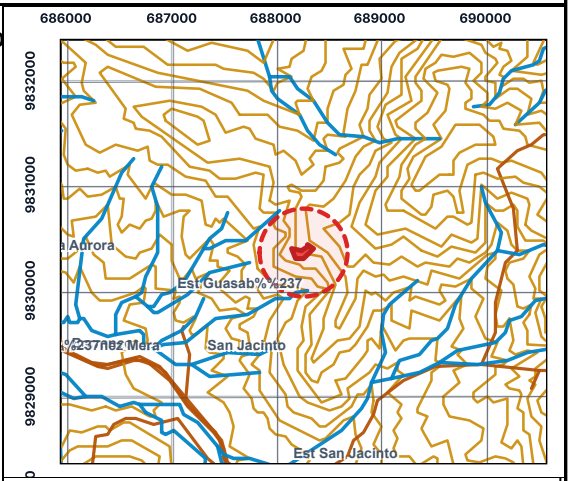

UBICACIÓN:

CARTA TOPOGRÁFICA: VENTANAS / CATARAMA / JUAN MONTALVO
CÓDIGO: NIV D1, 3789 IV / NIV D3, 3789 III / NIV F1, 3788 IV
ESCALA: 1:50000

POSESIONARIO:

DAVILA VELASCO ANGEL NEPTALI
C.C.: 1201427158

CODIGO CATASTRAL:

TEMP-315e4fb2

PROVINCIA:	**CANTÓN:**
LOS RIOS	URDANETA

PARROQUIA:

CATARAMA - URDANETA - PIJULLO

SECTOR:

SAN JACINTO

NOMBRE DEL PREDIO:

SIN NOMBRE

ESCALA GRÁFICA:

0 20 40 60 80 100Metros

FECHA:	**ÁREA:**	**ESCALA:**	**COORDENADAS PLANAS:**
15/10/2026	1.3687 Ha	~ 1:1400	SISTEMA DE COORDENADAS: WGS 1984 UTM ZONE 17S PROYECCIÓN: TRANSVERSE MERCATOR DATUM: WGS 1984

RESP. TÉCNICO:	**REVISADO Y APROBADO POR:**
	Ing. Mauricio Basantes Rodriguez

INFORME DE LINDERACIÓN

PROVINCIA:	CANTÓN:	PARROQUIA:	SECTOR:
Los Rios	Urdaneta	Catarama	SAN JACINTO

NOMBRES DEL POSESIONARIO	NOMBRE DEL PREDIO	CÓDIGO CATASTRAL
DAVILA VELASCO ANGEL NEPTALI C.C.: 1201427158	SIN NOMBRE	TEMP-315e4fb2

PUNTOS	COORDENADAS PLANAS UTM W.G.S.-84		VERTICE DESDE-HASTA	DISTANCIA (M)	RUMBO	COLINDANTES
	X	Y				
P01	688129.0	9830413.0	P01 - P02	4.1	N 75° 57' 50" E	-
P02	688133.0	9830414.0	P02 - P03	102.2	S 78° 8' 25" E	-
P03	688233.0	9830393.0	P03 - P04	45.8	N 58° 23' 33" E	-
P04	688272.0	9830417.0	P04 - P05	6.7	N 26° 33' 54" E	-
P05	688275.0	9830423.0	P05 - P06	9.4	N 32° 0' 19" E	-
P06	688280.0	9830431.0	P06 - P07	13.2	N 11° 30' 4" E	-
P07	688282.6	9830443.9	P07 - P08	77.8	S 66° 33' 44" E	-
P08	688354.0	9830413.0	P08 - P09	58.0	S 47° 47' 34" W	-
P09	688311.0	9830374.0	P09 - P10	42.7	S 57° 25' 33" W	-
P10	688275.0	9830351.0	P10 - P11	43.6	S 53° 23' 35" W	-
P11	688240.0	9830325.0	P11 - P12	68.8	S 84° 14' 34" W	-
P12	688171.6	9830318.1	P12 - P13	35.1	N 28° 13' 2" W	-
P13	688155.0	9830349.0	P13 - P01	69.1	N 22° 6' 34" W	-

DESCRIPCIÓN DE LINDEROS

COLINDANTE NORTE

Del P01 al P02 con una distancia de 4.1 m, Rumbo N 75° 57' 50" E
Del P02 al P03 con una distancia de 102.2 m, Rumbo S 78° 8' 25" E
Del P03 al P04 con una distancia de 45.8 m, Rumbo N 58° 23' 33" E
Del P04 al P05 con una distancia de 6.7 m, Rumbo N 26° 33' 54" E
Del P05 al P06 con una distancia de 9.4 m, Rumbo N 32° 0' 19" E
Del P06 al P07 con una distancia de 13.2 m, Rumbo N 11° 30' 4" E
Del P07 al P08 con una distancia de 77.8 m, Rumbo S 66° 33' 44" E

COLINDANTE SUR

Del P11 al P12 con una distancia de 68.8 m, Rumbo S 84° 14' 34" W

COLINDANTE ESTE

Del P08 al P09 con una distancia de 58.0 m, Rumbo S 47° 47' 34" W
Del P09 al P10 con una distancia de 42.7 m, Rumbo S 57° 25' 33" W
Del P10 al P11 con una distancia de 43.6 m, Rumbo S 53° 23' 35" W


COLINDANTE OESTE


Del P12 al P13 con una distancia de 35.1 m, Rumbo N 28° 13' 2" W
Del P13 al P01 con una distancia de 69.1 m, Rumbo N 22° 6' 34" W

RESPONSABILIDAD TÉCNICA	REVISADO Y APROBADO POR:
	Ing. Mauricio Basantes Rodriguez

GOBIERNO AUTÓNOMO DESCENTRALIZADO URDANETA.

LEVANTAMIENTO PLANIMÉTRICO

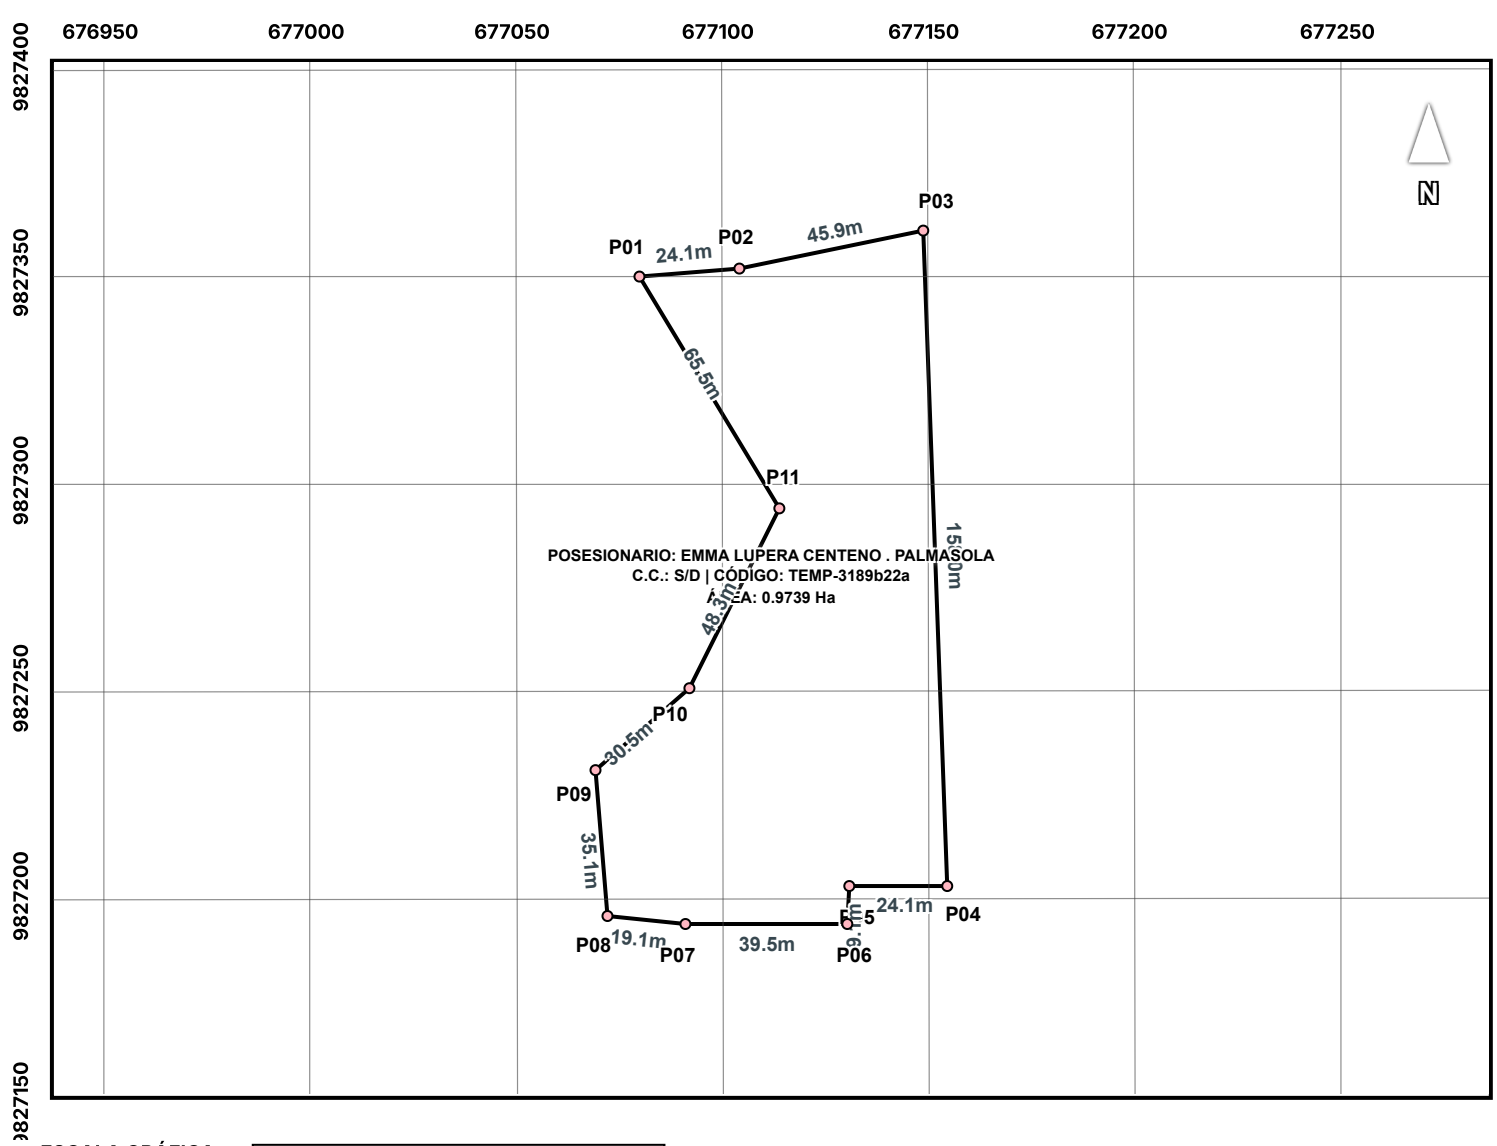

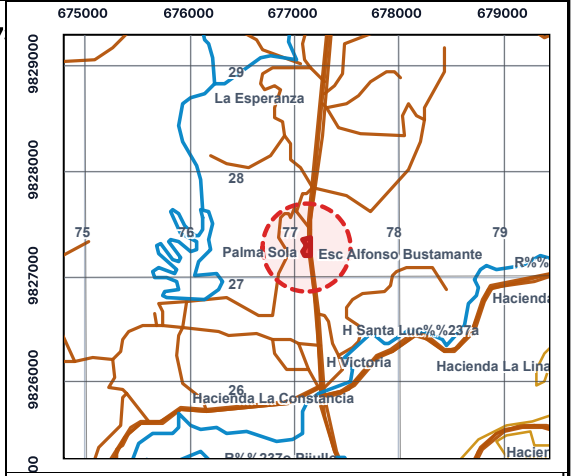

UBICACIÓN:

CARTA TOPOGRÁFICA: VENTANAS / CATARAMA / JUAN MONTALVO
CÓDIGO: NIV D1, 3789 IV / NIV D3, 3789 III / NIV F1, 3788 IV
ESCALA: 1:50000

POSESIONARIO:

EMMA LUPERA CENTENO . PALMASOLA
C.C.: S/D

CODIGO CATASTRAL:

TEMP-3189b22a

PROVINCIA:	**CANTÓN:**
LOS RIOS	URDANETA

PARROQUIA:

CATARAMA - URDANETA - PIJULLO

SECTOR:

RURAL

NOMBRE DEL PREDIO:

SIN NOMBRE

FECHA:	**ÁREA:**	**ESCALA:**	**COORDENADAS PLANAS:**
15/10/2026	0.9739 Ha	~ 1:1600	SISTEMA DE COORDENADAS: WGS 1984 UTM ZONE 17S PROYECCIÓN: TRANSVERSE MERCATOR DATUM: WGS 1984

RESP. TÉCNICO:	**REVISADO Y APROBADO POR:**
	Ing. Mauricio Basantes Rodriguez

INFORME DE LINDERACIÓN

PROVINCIA:	CANTÓN:	PARROQUIA:	SECTOR:
Los Rios	Urdaneta	Catarama	Rural

NOMBRES DEL POSESIONARIO	NOMBRE DEL PREDIO	CÓDIGO CATASTRAL
EMMA LUPERA CENTENO . PALMASOLA C.C.: S/D	SIN NOMBRE	TEMP-3189b22a

PUNTOS	COORDENADAS PLANAS UTM W.G.S.-84		VERTICE DESDE-HASTA	DISTANCIA (M)	RUMBO	COLINDANTES
	X	Y				
P01	677080.0	9827350.0	P01 - P02	24.1	N 89° 59' 10" W	-
P02	677104.0	9827352.0	P02 - P03	9.1	S 0° 27' 40" W	-
P03	677149.0	9827361.0	P03 - P04	39.5	S 90° 0' 0" W	-
P04	677154.7	9827203.1	P04 - P05	19.1	N 83° 59' 27" W	-
P05	677130.6	9827203.1	P05 - P06	35.1	N 4° 53' 57" W	-
P06	677130.5	9827194.0	P06 - P07	30.5	N 48° 59' 28" E	-
P07	677091.0	9827194.0	P07 - P08	48.3	N 27° 5' 44" E	-
P08	677072.0	9827196.0	P08 - P09	65.5	N 31° 15' 50" W	-
P09	677069.0	9827231.0	P09 - P10	24.1	N 85° 14' 10" E	-
P10	677092.0	9827251.0	P10 - P11	45.9	N 78° 41' 25" E	-
P11	677114.0	9827294.0	P11 - P01	158.0	S 2° 3' 28" E	-

DESCRIPCIÓN DE LINDEROS

COLINDANTE NORTE

Del P01 al P02 con una distancia de 24.1 m, Rumbo N 89° 59' 10" W
Del P02 al P03 con una distancia de 9.1 m, Rumbo S 0° 27' 40" W

COLINDANTE SUR

Del P04 al P05 con una distancia de 19.1 m, Rumbo N 83° 59' 27" W
Del P05 al P06 con una distancia de 35.1 m, Rumbo N 4° 53' 57" W
Del P06 al P07 con una distancia de 30.5 m, Rumbo N 48° 59' 28" E
Del P07 al P08 con una distancia de 48.3 m, Rumbo N 27° 5' 44" E

COLINDANTE ESTE

Del P03 al P04 con una distancia de 39.5 m, Rumbo S 90° 0' 0" W


COLINDANTE OESTE


Del P08 al P09 con una distancia de 65.5 m, Rumbo N 31° 15' 50" W
Del P09 al P10 con una distancia de 24.1 m, Rumbo N 85° 14' 10" E
Del P10 al P11 con una distancia de 45.9 m, Rumbo N 78° 41' 25" E
Del P11 al P01 con una distancia de 158.0 m, Rumbo S 2° 3' 28" E

RESPONSABILIDAD TÉCNICA	REVISADO Y APROBADO POR:
	Ing. Mauricio Basantes Rodriguez

GOBIERNO AUTÓNOMO DESCENTRALIZADO URDANETA.

LEVANTAMIENTO PLANIMÉTRICO

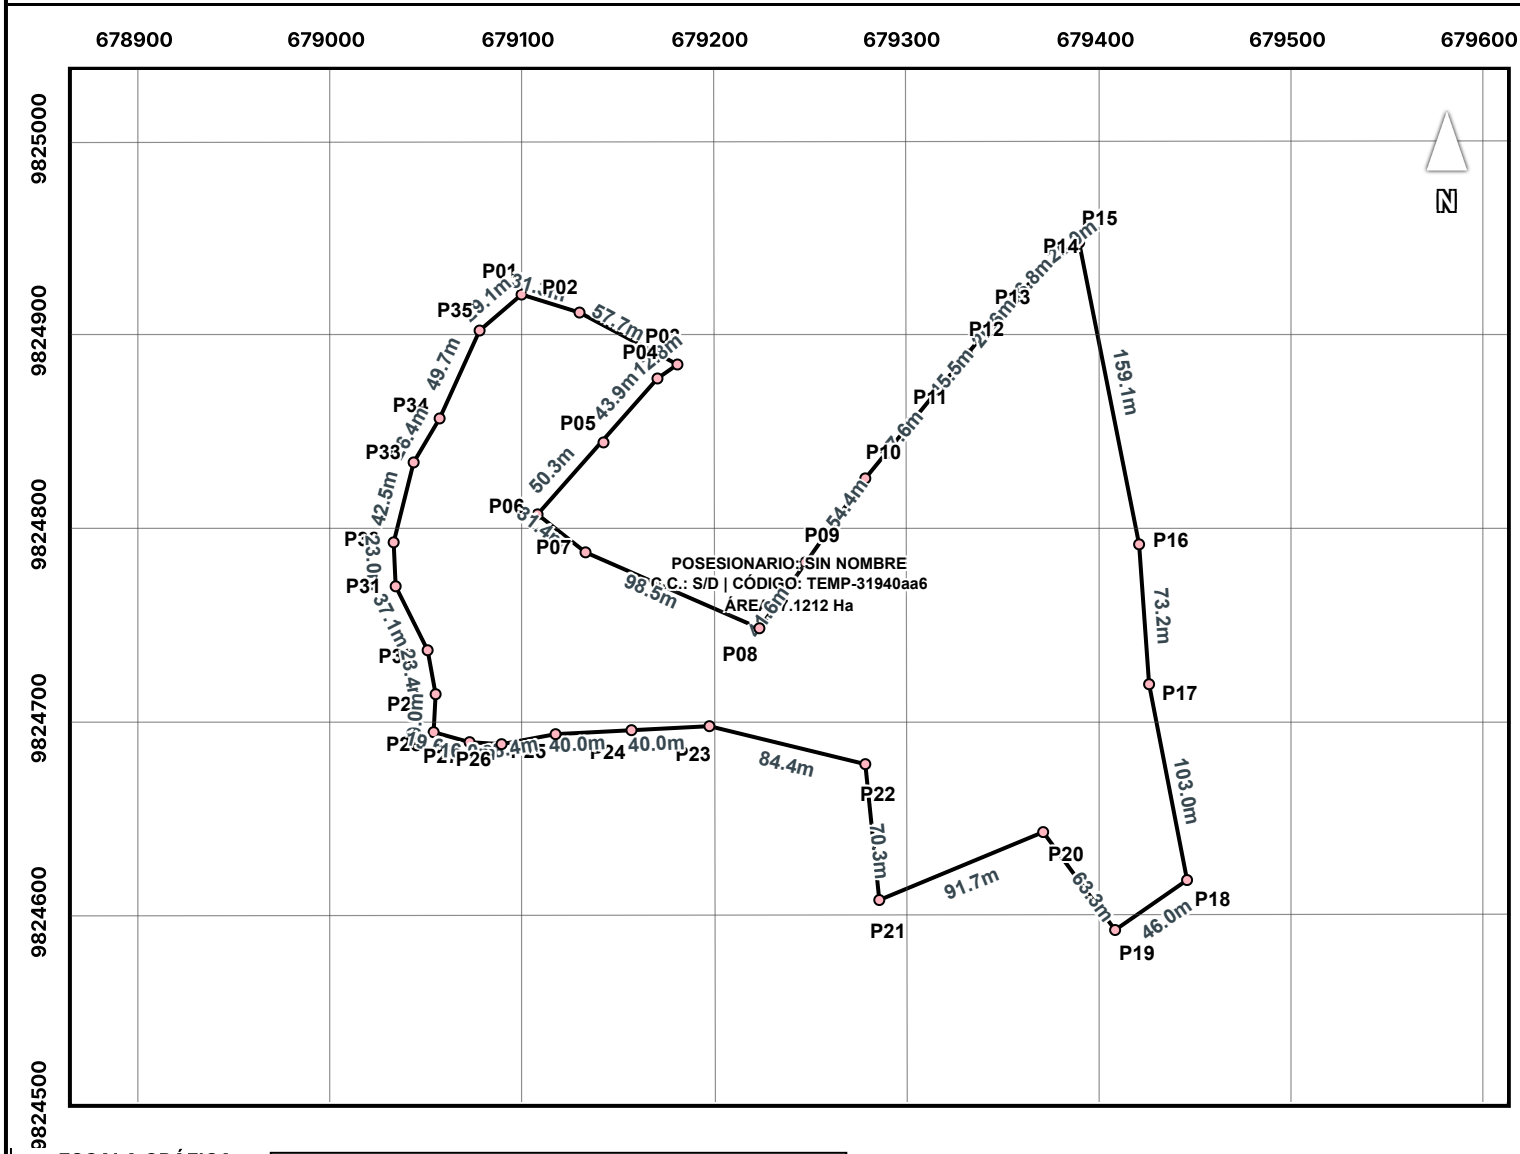

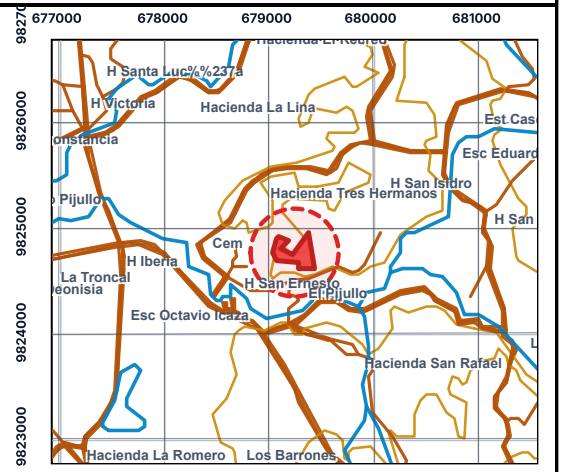

UBICACIÓN:

CARTA TOPOGRÁFICA: VENTANAS / CATARAMA / JUAN MONTALVO
CÓDIGO: NIV D1, 3789 IV / NIV D3, 3789 III / NIV F1, 3788 IV
ESCALA: 1:50000

POSESIONARIO:

SIN NOMBRE
C.C.: S/D

CODIGO CATASTRAL:

TEMP-31940aa6

PROVINCIA:	**CANTÓN:**
LOS RIOS	URDANETA

PARROQUIA:

CATARAMA - URDANETA - PIJULLO

SECTOR:

RURAL

NOMBRE DEL PREDIO:

SIN NOMBRE

FECHA:	**ÁREA:**	**ESCALA:**	**COORDENADAS PLANAS:**
15/10/2026	7.1212 Ha	~ 1:3500	SISTEMA DE COORDENADAS: WGS 1984 UTM ZONE 17S PROYECCIÓN: TRANSVERSE MERCATOR DATUM: WGS 1984

RESP. TÉCNICO:	**REVISADO Y APROBADO POR:**
	Ing. Mauricio Basantes Rodriguez

INFORME DE LINDERACIÓN (HOJA 1 DE 2)

PROVINCIA:	CANTÓN:	PARROQUIA:	SECTOR:
Los Rios	Urdaneta	Catarama	Rural

NOMBRES DEL POSESIONARIO	NOMBRE DEL PREDIO	CÓDIGO CATASTRAL
SIN NOMBRE C.C.: S/D	SIN NOMBRE	TEMP-31940aa6

PUNTOS	COORDENADAS PLANAS UTM W.G.S.-84		VERTICE DESDE-HASTA	DISTANCIA (M)	RUMBO	COLINDANTES
	X	Y				
P01	679100.0	9824921.0	P01 - P02	50.3	S 42° 34' 50" W	-
P02	679130.0	9824912.0	P02 - P03	31.4	S 52° 45' 55" E	-
P03	679181.0	9824885.0	P03 - P04	98.5	S 66° 2' 15" E	-
P04	679171.0	9824877.0	P04 - P05	41.6	N 35° 13' 3" E	-
P05	679142.0	9824844.0	P05 - P06	54.4	N 36° 1' 39" E	-
P06	679108.0	9824807.0	P06 - P07	37.6	N 39° 36' 38" E	-
P07	679133.0	9824788.0	P07 - P08	45.5	N 39° 38' 39" E	-
P08	679223.0	9824748.0	P08 - P09	20.6	N 39° 5' 38" E	-
P09	679247.0	9824782.0	P09 - P10	36.8	N 42° 47' 51" E	-
P10	679279.0	9824826.0	P10 - P11	25.0	N 53° 7' 48" E	-
P11	679303.0	9824855.0	P11 - P12	159.1	S 11° 14' 21" E	-
P12	679332.0	9824890.0	P12 - P13	73.2	S 3° 55' 6" E	-
P13	679345.0	9824906.0	P13 - P14	103.0	S 11° 12' 3" E	-
P14	679370.0	9824933.0	P14 - P15	46.0	S 55° 37' 11" W	-
P15	679390.0	9824948.0	P15 - P16	63.3	N 36° 5' 37" W	-
P16	679421.0	9824792.0	P16 - P17	91.7	S 67° 29' 37" W	-
P17	679426.0	9824719.0	P17 - P18	70.3	N 5° 42' 38" W	-
P18	679446.0	9824618.0	P18 - P19	84.4	N 76° 17' 35" W	-
P19	679408.0	9824592.0	P19 - P20	40.0	S 87° 8' 15" W	-
P20	679370.7	9824643.1	P20 - P21	40.0	S 87° 8' 15" W	-
P21	679286.0	9824608.0	P21 - P22	28.4	S 79° 52' 31" W	-
P22	679279.0	9824678.0	P22 - P23	16.0	N 86° 25' 25" W	-
P23	679197.0	9824698.0	P23 - P24	19.6	N 75° 15' 23" W	-
P24	679157.0	9824696.0	P24 - P25	19.0	N 3° 0' 46" E	-
P25	679117.0	9824694.0	P25 - P26	23.4	N 9° 51' 57" W	-
P26	679089.0	9824689.0	P26 - P27	37.1	N 27° 15' 19" W	-
P27	679073.0	9824690.0	P27 - P28	23.0	N 2° 29' 22" W	-
P28	679054.0	9824695.0	P28 - P29	42.5	N 15° 1' 6" E	-

DESCRIPCIÓN DE LINDEROS (HOJA 1 DE 2)

COLINDANTE NORTE

Del P01 al P02 con una distancia de 50.3 m, Rumbo S 42° 34' 50" W
Del P02 al P03 con una distancia de 31.4 m, Rumbo S 52° 45' 55" E
Del P03 al P04 con una distancia de 98.5 m, Rumbo S 66° 2' 15" E
Del P04 al P05 con una distancia de 41.6 m, Rumbo N 35° 13' 3" E
Del P05 al P06 con una distancia de 54.4 m, Rumbo N 36° 1' 39" E
Del P06 al P07 con una distancia de 37.6 m, Rumbo N 39° 36' 38" E
Del P07 al P08 con una distancia de 45.5 m, Rumbo N 39° 38' 39" E
Del P08 al P09 con una distancia de 20.6 m, Rumbo N 39° 5' 38" E
Del P09 al P10 con una distancia de 36.8 m, Rumbo N 42° 47' 51" E
Del P10 al P11 con una distancia de 25.0 m, Rumbo N 53° 7' 48" E
Del P11 al P12 con una distancia de 159.1 m, Rumbo S 11° 14' 21" E
Del P12 al P13 con una distancia de 73.2 m, Rumbo S 3° 55' 6" E
Del P13 al P14 con una distancia de 103.0 m, Rumbo S 11° 12' 3" E
Del P14 al P15 con una distancia de 46.0 m, Rumbo S 55° 37' 11" W

COLINDANTE SUR

Del P18 al P19 con una distancia de 84.4 m, Rumbo N 76° 17' 35" W
Del P19 al P20 con una distancia de 40.0 m, Rumbo S 87° 8' 15" W
Del P20 al P21 con una distancia de 40.0 m, Rumbo S 87° 8' 15" W
Del P21 al P22 con una distancia de 28.4 m, Rumbo S 79° 52' 31" W
Del P22 al P23 con una distancia de 16.0 m, Rumbo N 86° 25' 25" W
Del P23 al P24 con una distancia de 19.6 m, Rumbo N 75° 15' 23" W
Del P24 al P25 con una distancia de 19.0 m, Rumbo N 3° 0' 46" E
Del P25 al P26 con una distancia de 23.4 m, Rumbo N 9° 51' 57" W
Del P26 al P27 con una distancia de 37.1 m, Rumbo N 27° 15' 19" W
Del P27 al P28 con una distancia de 23.0 m, Rumbo N 2° 29' 22" W

COLINDANTE ESTE

Del P15 al P16 con una distancia de 63.3 m, Rumbo N 36° 5' 37" W
Del P16 al P17 con una distancia de 91.7 m, Rumbo S 67° 29' 37" W
Del P17 al P18 con una distancia de 70.3 m, Rumbo N 5° 42' 38" W

COLINDANTE OESTE

Del P28 al P29 con una distancia de 42.5 m, Rumbo N 15° 1' 6" E
Del P29 al P30 con una distancia de 26.4 m, Rumbo N 29° 28' 33" E
Del P30 al P31 con una distancia de 49.7 m, Rumbo N 25° 1' 1" E
Del P31 al P32 con una distancia de 29.1 m, Rumbo N 49° 11' 6" E
Del P32 al P33 con una distancia de 31.3 m, Rumbo S 73° 18' 3" E
Del P33 al P34 con una distancia de 57.7 m, Rumbo S 62° 6' 10" E
Del P34 al P35 con una distancia de 12.8 m, Rumbo S 51° 20' 25" W
Del P35 al P01 con una distancia de 43.9 m, Rumbo S 41° 18' 31" W

INFORME DE LINDERACIÓN (HOJA 2 DE 2)

PROVINCIA:	CANTÓN:	PARROQUIA:	SECTOR:
Los Rios	Urdaneta	Catarama	Rural

NOMBRES DEL POSESIONARIO	NOMBRE DEL PREDIO	CÓDIGO CATASTRAL
SIN NOMBRE C.C.: S/D	SIN NOMBRE	TEMP-31940aa6

PUNTOS	COORDENADAS PLANAS UTM W.G.S.-84		VERTICE DESDE-HASTA	DISTANCIA (M)	RUMBO	COLINDANTES
	X	Y				
P29	679055.0	9824714.0	P29 - P30	26.4	N 29° 28' 33" E	-
P30	679051.0	9824737.0	P30 - P31	49.7	N 25° 1' 1" E	-
P31	679034.0	9824770.0	P31 - P32	29.1	N 49° 11' 6" E	-
P32	679033.0	9824793.0	P32 - P33	31.3	S 73° 18' 3" E	-
P33	679044.0	9824834.0	P33 - P34	57.7	S 62° 6' 10" E	-
P34	679057.0	9824857.0	P34 - P35	12.8	S 51° 20' 25" W	-
P35	679078.0	9824902.0	P35 - P01	43.9	S 41° 18' 31" W	-


DESCRIPCIÓN DE LINDEROS (HOJA 2 DE 2)

(Descripción de linderos completada en láminas anteriores)

RESPONSABILIDAD TÉCNICA	REVISADO Y APROBADO POR:
	Ing. Mauricio Basantes Rodriguez


GOBIERNO AUTÓNOMO DESCENTRALIZADO URDANETA.

LEVANTAMIENTO PLANIMÉTRICO

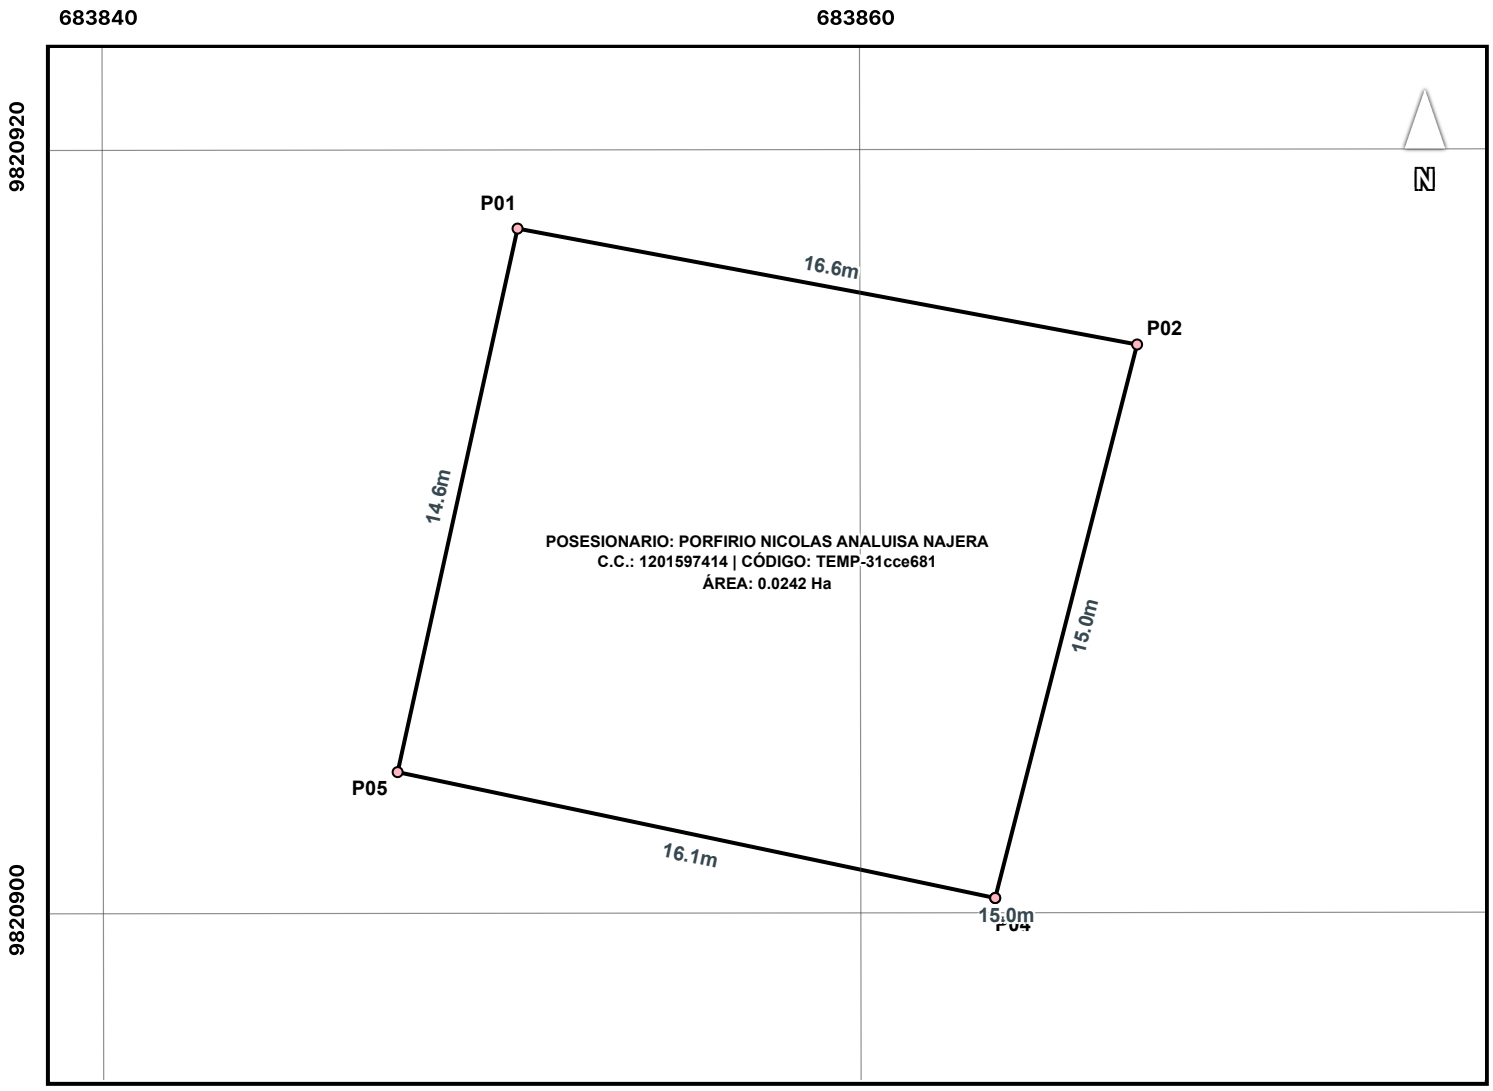

ESCALA GRÁFICA: 0 2 4 6 8 10 Metros

FECHA:	ÁREA:	ESCALA:	COORDENADAS PLANAS:
15/10/2026	0.0242 Ha	~ 1:200	SISTEMA DE COORDENADAS: WGS 1984 UTM ZONE 17S PROYECCIÓN: TRANSVERSE MERCATOR DATUM: WGS 1984

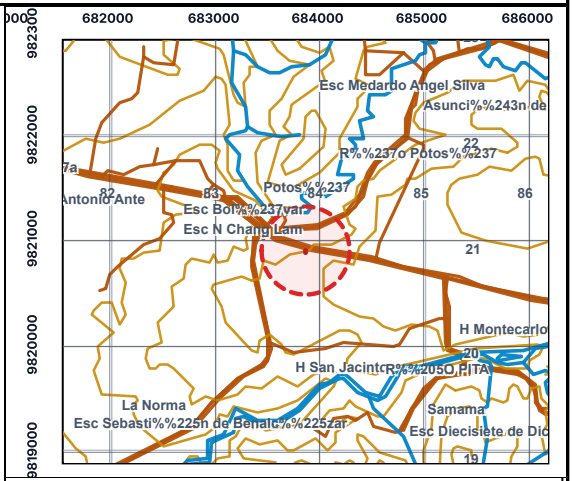

UBICACIÓN:

CARTA TOPOGRÁFICA: VENTANAS / CATARAMA / JUAN MONTALVO
CÓDIGO: NIV D1, 3789 IV / NIV D3, 3789 III / NIV F1, 3788 IV
ESCALA: 1:50000

POSESIONARIO:

PORFIRIO NICOLAS ANALUISA NAJERA
C.C.: 1201597414

CODIGO CATASTRAL:

TEMP-31cce681

PROVINCIA:	CANTÓN:
LOS RIOS	URDANETA

PARROQUIA:

CATARAMA - URDANETA - PIJULLO

SECTOR:

POTOSI

NOMBRE DEL PREDIO:

SIN NOMBRE

RESP. TÉCNICO:	REVISADO Y APROBADO POR:
	Ing. Mauricio Basantes Rodriguez

INFORME DE LINDERACIÓN

PROVINCIA:	CANTÓN:	PARROQUIA:	SECTOR:
Los Rios	Urdaneta	Catarama	POTOSI

NOMBRES DEL POSESIONARIO	NOMBRE DEL PREDIO	CÓDIGO CATASTRAL
PORFIRIO NICOLAS ANALUISA NAJERA C.C.: 1201597414	SIN NOMBRE	TEMP-31cce681

PUNTOS	COORDENADAS PLANAS UTM W.G.S.-84		VERTICE DESDE-HASTA	DISTANCIA (M)	RUMBO	COLINDANTES
	X	Y				
P01	683851.0	9820917.9	P01 - P02	15.0	S 14° 35' 17" W	-
P02	683867.3	9820914.9	P02 - P03	15.0	S 14° 35' 18" W	-
P03	683863.6	9820900.3	P03 - P04	16.1	N 77° 57' 1" W	-
P04	683863.6	9820900.3	P04 - P05	14.6	N 12° 31' 48" E	-
P05	683847.8	9820903.7	P05 - P01	16.6	S 79° 27' 39" E	-

DESCRIPCIÓN DE LINDEROS

COLINDANTE NORTE

Del P01 al P02 con una distancia de 15.0 m, Rumbo S 14° 35' 17" W

COLINDANTE SUR

Del P03 al P04 con una distancia de 16.1 m, Rumbo N 77° 57' 1" W
Del P04 al P05 con una distancia de 14.6 m, Rumbo N 12° 31' 48" E

COLINDANTE ESTE

Del P02 al P03 con una distancia de 15.0 m, Rumbo S 14° 35' 18" W


COLINDANTE OESTE


Del P05 al P01 con una distancia de 16.6 m, Rumbo S 79° 27' 39" E

RESPONSABILIDAD TÉCNICA	REVISADO Y APROBADO POR:
	Ing. Mauricio Basantes Rodriguez

GOBIERNO AUTÓNOMO DESCENTRALIZADO URDANETA.

LEVANTAMIENTO PLANIMÉTRICO

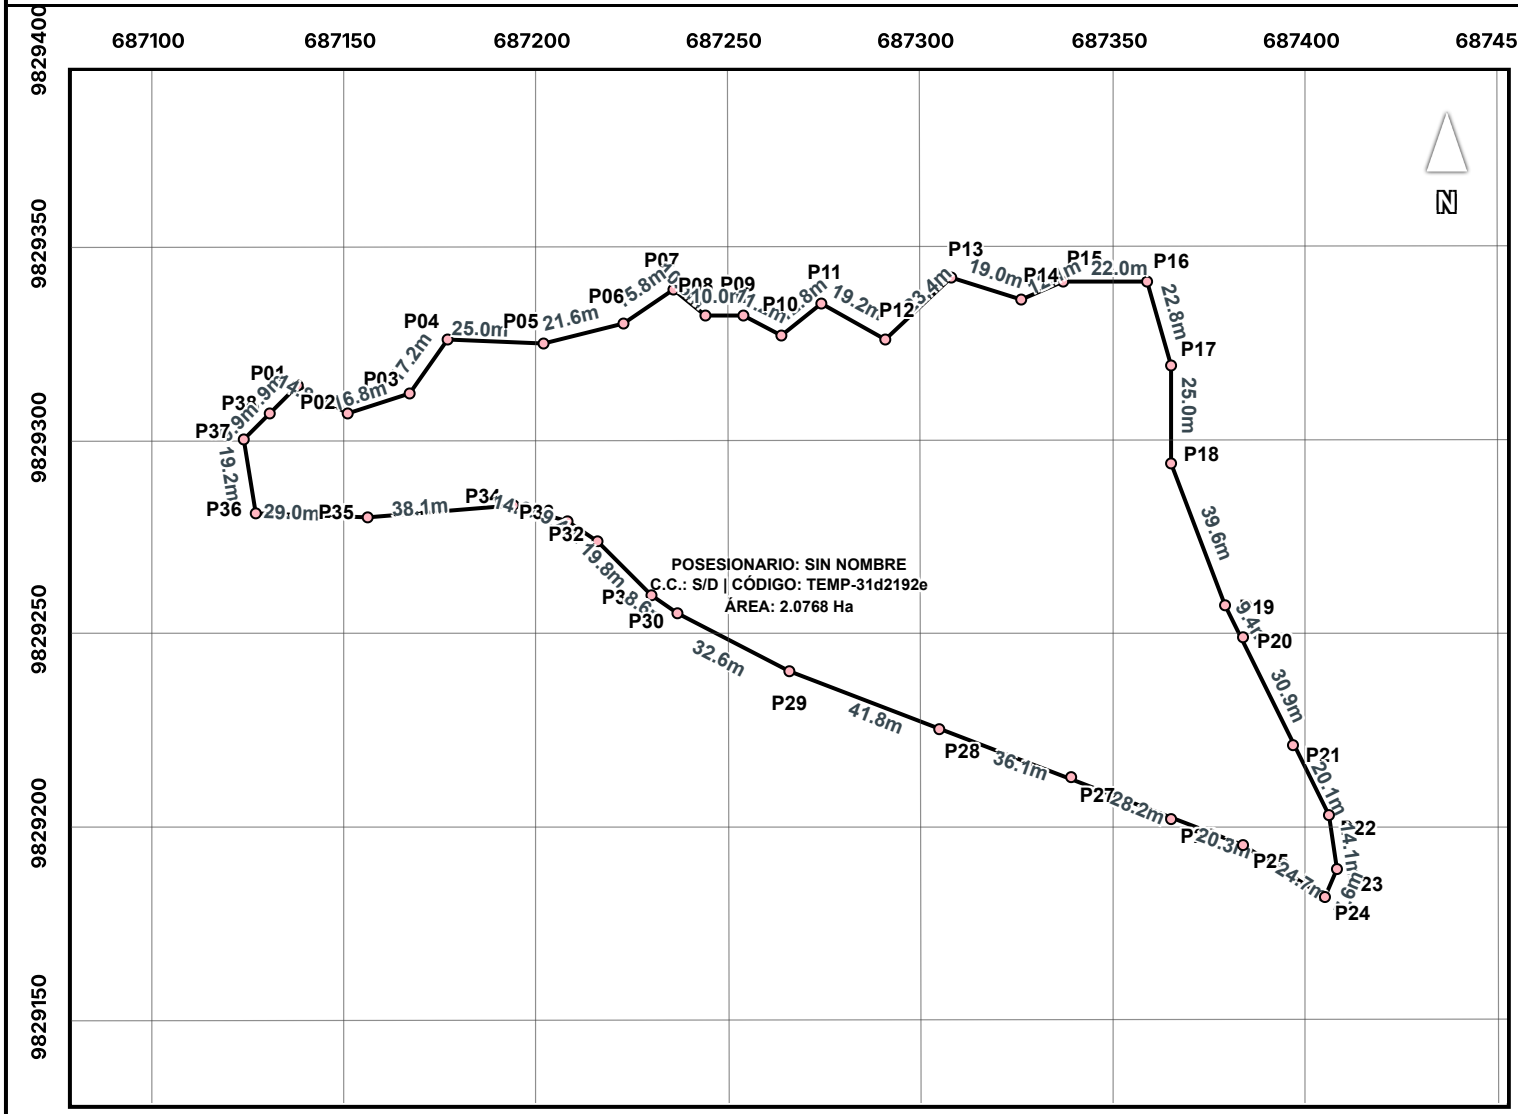

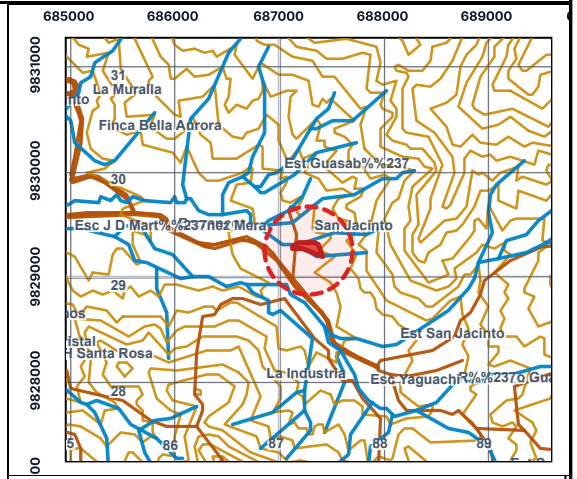

UBICACIÓN:

CARTA TOPOGRÁFICA: VENTANAS / CATARAMA / JUAN MONTALVO
CÓDIGO: NIV D1, 3789 IV / NIV D3, 3789 III / NIV F1, 3788 IV
ESCALA: 1:50000

POSESIONARIO:

SIN NOMBRE
C.C.: S/D

CODIGO CATASTRAL:

TEMP-31d2192e

PROVINCIA:	**CANTÓN:**
LOS RIOS	URDANETA

PARROQUIA:

CATARAMA - URDANETA - PIJULLO

SECTOR:

LA INDUSTRIA

NOMBRE DEL PREDIO:

SIN NOMBRE

FECHA:	**ÁREA:**	**ESCALA:**	**COORDENADAS PLANAS:**
15/10/2026	2.0768 Ha	~ 1:1700	SISTEMA DE COORDENADAS: WGS 1984 UTM ZONE 17S PROYECCIÓN: TRANSVERSE MERCATOR DATUM: WGS 1984

RESP. TÉCNICO:	**REVISADO Y APROBADO POR:**
	Ing. Mauricio Basantes Rodriguez

INFORME DE LINDERACIÓN (HOJA 1 DE 2)

PROVINCIA:	CANTÓN:	PARROQUIA:	SECTOR:
Los Rios	Urdaneta	Catarama	LA INDUSTRIA

NOMBRES DEL POSESIONARIO	NOMBRE DEL PREDIO	CÓDIGO CATASTRAL
SIN NOMBRE C.C.: S/D	SIN NOMBRE	TEMP-31d2192e

PUNTOS	COORDENADAS PLANAS UTM W.G.S.-84		VERTICE DESDE-HASTA	DISTANCIA (M)	RUMBO	COLINDANTES
	X	Y				
P01	687138.0	9829314.0	P01 - P02	17.2	N 35° 32' 16" E	-
P02	687151.0	9829307.0	P02 - P03	25.0	S 87° 42' 34" E	-
P03	687167.0	9829312.0	P03 - P04	21.6	N 76° 36' 27" E	-
P04	687177.0	9829326.0	P04 - P05	15.8	N 55° 18' 17" E	-
P05	687202.0	9829325.0	P05 - P06	10.6	S 48° 48' 51" E	-
P06	687223.0	9829330.0	P06 - P07	10.0	N 90° 0' 0" E	-
P07	687236.0	9829339.0	P07 - P08	11.2	S 63° 26' 6" E	-
P08	687244.0	9829332.0	P08 - P09	12.8	N 51° 20' 25" E	-
P09	687254.0	9829332.0	P09 - P10	19.2	S 62° 6' 10" E	-
P10	687264.0	9829327.0	P10 - P11	23.4	N 46° 44' 9" E	-
P11	687274.0	9829335.0	P11 - P12	19.0	S 71° 33' 54" E	-
P12	687291.0	9829326.0	P12 - P13	12.1	N 65° 33' 22" E	-
P13	687308.0	9829342.0	P13 - P14	22.0	N 90° 0' 0" E	-
P14	687326.0	9829336.0	P14 - P15	22.8	S 15° 15' 18" E	-
P15	687337.0	9829341.0	P15 - P16	25.0	S 0° 0' 0" E	-
P16	687359.0	9829341.0	P16 - P17	39.6	S 20° 43' 32" E	-
P17	687365.0	9829319.0	P17 - P18	9.4	S 32° 0' 19" E	-
P18	687365.0	9829294.0	P18 - P19	30.9	S 24° 54' 17" E	-
P19	687379.0	9829257.0	P19 - P20	20.1	S 26° 33' 54" E	-
P20	687384.0	9829249.0	P20 - P21	14.1	S 8° 7' 48" E	-
P21	687397.0	9829221.0	P21 - P22	7.6	S 23° 11' 55" W	-
P22	687406.0	9829203.0	P22 - P23	24.7	N 58° 14' 26" W	-
P23	687408.0	9829189.0	P23 - P24	20.3	N 69° 46' 31" W	-
P24	687405.0	9829182.0	P24 - P25	28.2	N 67° 4' 4" W	-
P25	687384.0	9829195.0	P25 - P26	36.1	N 70° 33' 36" W	-
P26	687365.0	9829202.0	P26 - P27	41.8	N 68° 57' 45" W	-
P27	687339.0	9829213.0	P27 - P28	32.6	N 62° 39' 0" W	-
P28	687305.0	9829225.0	P28 - P29	8.6	N 54° 27' 44" W	-

DESCRIPCIÓN DE LINDEROS (HOJA 1 DE 2)

COLINDANTE NORTE

Del P01 al P02 con una distancia de 17.2 m, Rumbo N 35° 32' 16" E
Del P02 al P03 con una distancia de 25.0 m, Rumbo S 87° 42' 34" E
Del P03 al P04 con una distancia de 21.6 m, Rumbo N 76° 36' 27" E
Del P04 al P05 con una distancia de 15.8 m, Rumbo N 55° 18' 17" E
Del P05 al P06 con una distancia de 10.6 m, Rumbo S 48° 48' 51" E
Del P06 al P07 con una distancia de 10.0 m, Rumbo N 90° 0' 0" E
Del P07 al P08 con una distancia de 11.2 m, Rumbo S 63° 26' 6" E
Del P08 al P09 con una distancia de 12.8 m, Rumbo N 51° 20' 25" E
Del P09 al P10 con una distancia de 19.2 m, Rumbo S 62° 6' 10" E
Del P10 al P11 con una distancia de 23.4 m, Rumbo N 46° 44' 9" E
Del P11 al P12 con una distancia de 19.0 m, Rumbo S 71° 33' 54" E
Del P12 al P13 con una distancia de 12.1 m, Rumbo N 65° 33' 22" E
Del P13 al P14 con una distancia de 22.0 m, Rumbo N 90° 0' 0" E
Del P14 al P15 con una distancia de 22.8 m, Rumbo S 15° 15' 18" E
Del P15 al P16 con una distancia de 25.0 m, Rumbo S 0° 0' 0" E

COLINDANTE SUR

Del P24 al P25 con una distancia de 28.2 m, Rumbo N 67° 4' 4" W
Del P25 al P26 con una distancia de 36.1 m, Rumbo N 70° 33' 36" W
Del P26 al P27 con una distancia de 41.8 m, Rumbo N 68° 57' 45" W
Del P27 al P28 con una distancia de 32.6 m, Rumbo N 62° 39' 0" W
Del P28 al P29 con una distancia de 8.6 m, Rumbo N 54° 27' 44" W
Del P29 al P30 con una distancia de 19.8 m, Rumbo N 45° 0' 0" W
Del P30 al P31 con una distancia de 9.4 m, Rumbo N 57° 59' 41" W
Del P31 al P32 con una distancia de 14.6 m, Rumbo N 74° 3' 17" W
Del P32 al P33 con una distancia de 38.1 m, Rumbo S 85° 29' 10" W
Del P33 al P34 con una distancia de 29.0 m, Rumbo N 88° 1' 30" W
Del P34 al P35 con una distancia de 19.2 m, Rumbo N 8° 58' 21" W
Del P35 al P36 con una distancia de 9.9 m, Rumbo N 45° 0' 0" E

COLINDANTE ESTE

Del P16 al P17 con una distancia de 39.6 m, Rumbo S 20° 43' 32" E
Del P17 al P18 con una distancia de 9.4 m, Rumbo S 32° 0' 19" E
Del P18 al P19 con una distancia de 30.9 m, Rumbo S 24° 54' 17" E
Del P19 al P20 con una distancia de 20.1 m, Rumbo S 26° 33' 54" E
Del P20 al P21 con una distancia de 14.1 m, Rumbo S 8° 7' 48" E
Del P21 al P22 con una distancia de 7.6 m, Rumbo S 23° 11' 55" W
Del P22 al P23 con una distancia de 24.7 m, Rumbo N 58° 14' 26" W
Del P23 al P24 con una distancia de 20.3 m, Rumbo N 69° 46' 31" W

COLINDANTE OESTE

Del P36 al P37 con una distancia de 9.9 m, Rumbo N 45° 0' 0" E
Del P37 al P38 con una distancia de 14.8 m, Rumbo S 61° 41' 57" E
Del P38 al P01 con una distancia de 16.8 m, Rumbo N 72° 38' 46" E

INFORME DE LINDERACIÓN (HOJA 2 DE 2)

PROVINCIA:	CANTÓN:	PARROQUIA:	SECTOR:
Los Rios	Urdaneta	Catarama	LA INDUSTRIA

NOMBRES DEL POSESIONARIO	NOMBRE DEL PREDIO	CÓDIGO CATASTRAL
SIN NOMBRE C.C.: S/D	SIN NOMBRE	TEMP-31d2192e

PUNTOS	COORDENADAS PLANAS UTM W.G.S.-84		VERTICE DESDE-HASTA	DISTANCIA (M)	RUMBO	COLINDANTES
	X	Y				
P29	687266.0	9829240.0	P29 - P30	19.8	N 45° 0' 0" W	-
P30	687237.0	9829255.0	P30 - P31	9.4	N 57° 59' 41" W	-
P31	687230.0	9829260.0	P31 - P32	14.6	N 74° 3' 17" W	-
P32	687216.0	9829274.0	P32 - P33	38.1	S 85° 29' 10" W	-
P33	687208.0	9829279.0	P33 - P34	29.0	N 88° 1' 30" W	-
P34	687194.0	9829283.0	P34 - P35	19.2	N 8° 58' 21" W	-
P35	687156.0	9829280.0	P35 - P36	9.9	N 45° 0' 0" E	-
P36	687127.0	9829281.0	P36 - P37	9.9	N 45° 0' 0" E	-
P37	687124.0	9829300.0	P37 - P38	14.8	S 61° 41' 57" E	-
P38	687131.0	9829307.0	P38 - P01	16.8	N 72° 38' 46" E	-

DESCRIPCIÓN DE LINDEROS (HOJA 2 DE 2)

(Descripción de linderos completada en láminas anteriores)

RESPONSABILIDAD TÉCNICA	REVISADO Y APROBADO POR:
	Ing. Mauricio Basantes Rodriguez