

GOBIERNO AUTÓNOMO DESCENTRALIZADO URDANETA.

LEVANTAMIENTO PLANIMÉTRICO

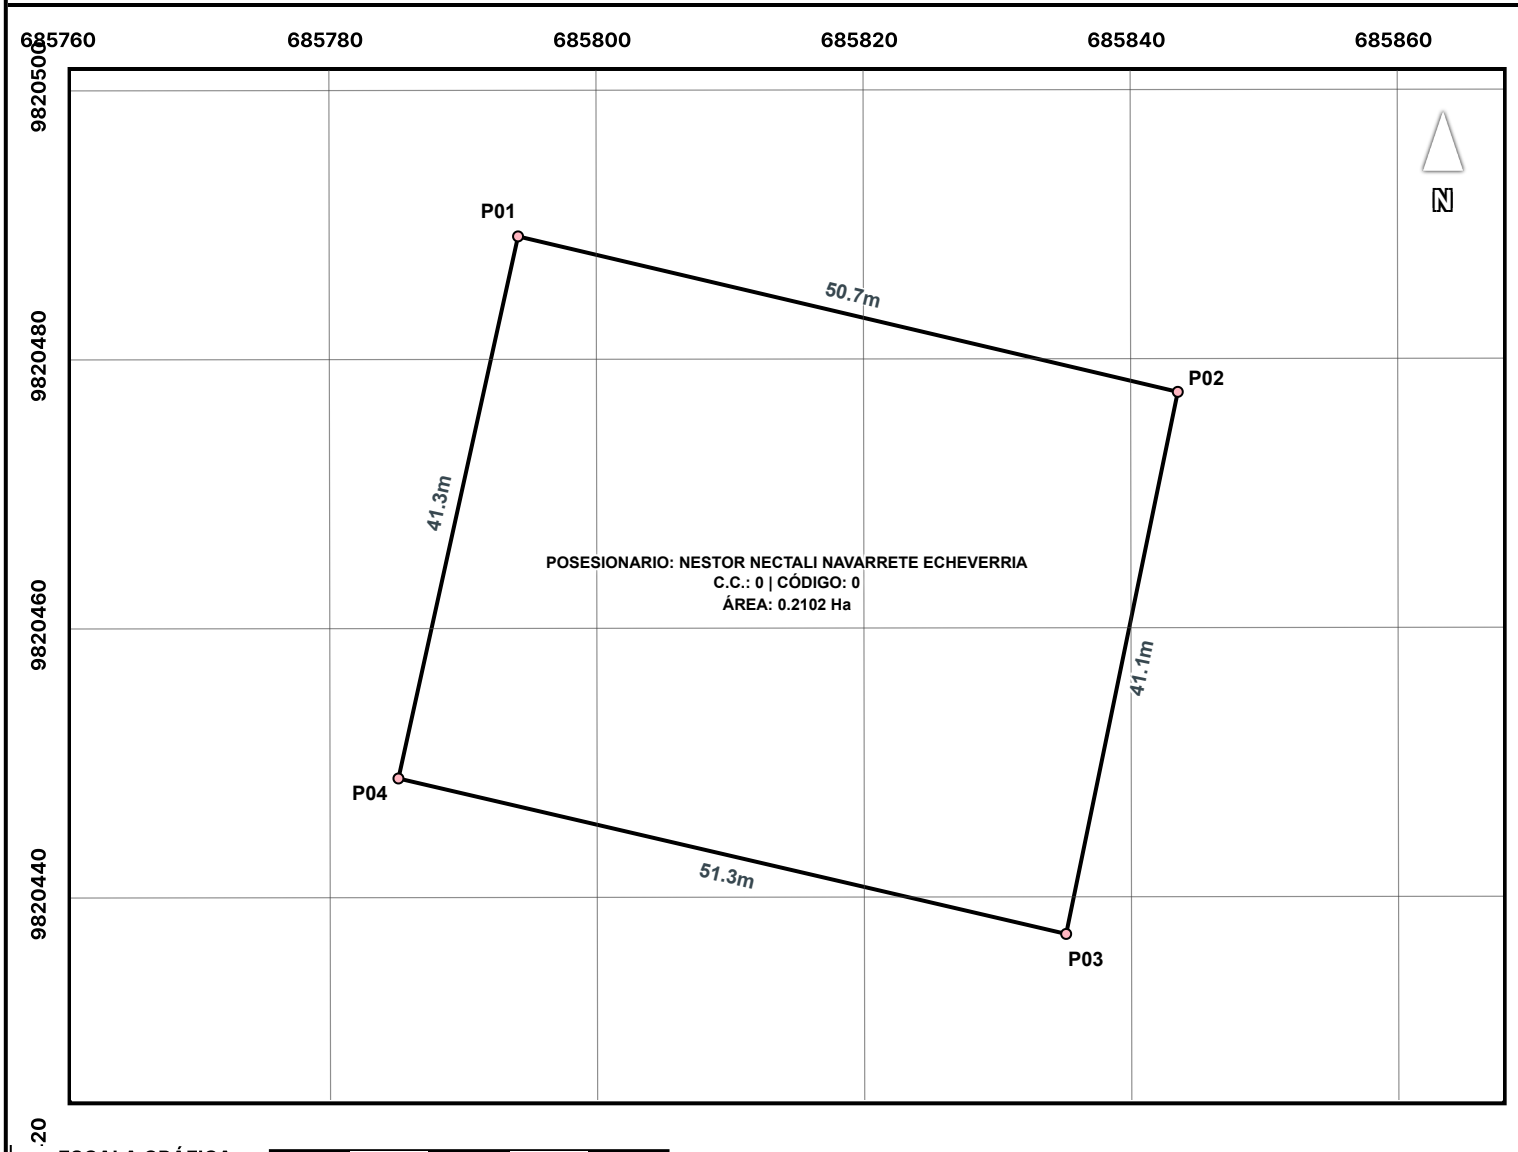

ESCALA GRÁFICA: 0 6 12 18 24 30 Metros

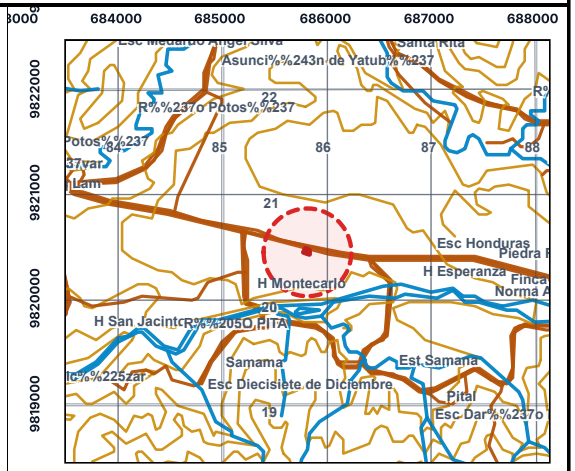

UBICACIÓN:

CARTA TOPOGRÁFICA: VENTANAS / CATARAMA / JUAN MONTALVO
CÓDIGO: NIV D1, 3789 IV / NIV D3, 3789 III / NIV F1, 3788 IV
ESCALA: 1:50000

POSESIONARIO:

NESTOR NECTALI NAVARRETE ECHEVERRIA
C.C.: 0

CODIGO CATASTRAL:

0

PROVINCIA:	**CANTÓN:**
LOS RIOS	URDANETA

PARROQUIA:

CATARAMA - URDANETA - PIJULLO

SECTOR:

RURAL

NOMBRE DEL PREDIO:

SIN NOMBRE

FECHA:	**ÁREA:**	**ESCALA:**	**COORDENADAS PLANAS:**
15/10/2026	0.2102 Ha	~ 1:500	SISTEMA DE COORDENADAS: WGS 1984 UTM ZONE 17S PROYECCIÓN: TRANSVERSE MERCATOR DATUM: WGS 1984

RESP. TÉCNICO:	**REVISADO Y APROBADO POR:**
	Ing. Mauricio Basantes Rodriguez

INFORME DE LINDERACIÓN

PROVINCIA:	CANTÓN:	PARROQUIA:	SECTOR:
Los Rios	Urdaneta	Catarama	Rural

NOMBRES DEL POSESIONARIO	NOMBRE DEL PREDIO	CÓDIGO CATASTRAL
NESTOR NECTALI NAVARRETE ECHEVERRIA C.C.: 0	SIN NOMBRE	0

PUNTOS	COORDENADAS PLANAS UTM W.G.S.-84		VERTICE DESDE-HASTA	DISTANCIA (M)	RUMBO	COLINDANTES
	X	Y				
P01	685794.2	9820489.2	P01 - P02	41.1	S 11° 47' 14" W	-
P02	685843.5	9820477.5	P02 - P03	51.3	N 76° 54' 19" W	-
P03	685835.1	9820437.3	P03 - P04	41.3	N 12° 36' 28" E	-
P04	685785.1	9820448.9	P04 - P01	50.7	S 76° 37' 5" E	-

DESCRIPCIÓN DE LINDEROS

COLINDANTE NORTE

Del P01 al P02 con una distancia de 41.1 m, Rumbo S 11° 47' 14" W

COLINDANTE SUR

Del P03 al P04 con una distancia de 41.3 m, Rumbo N 12° 36' 28" E

COLINDANTE ESTE

Del P02 al P03 con una distancia de 51.3 m, Rumbo N 76° 54' 19" W

COLINDANTE OESTE

Del P04 al P01 con una distancia de 50.7 m, Rumbo S 76° 37' 5" E

RESPONSABILIDAD TÉCNICA	REVISADO Y APROBADO POR:
	Ing. Mauricio Basantes Rodriguez